




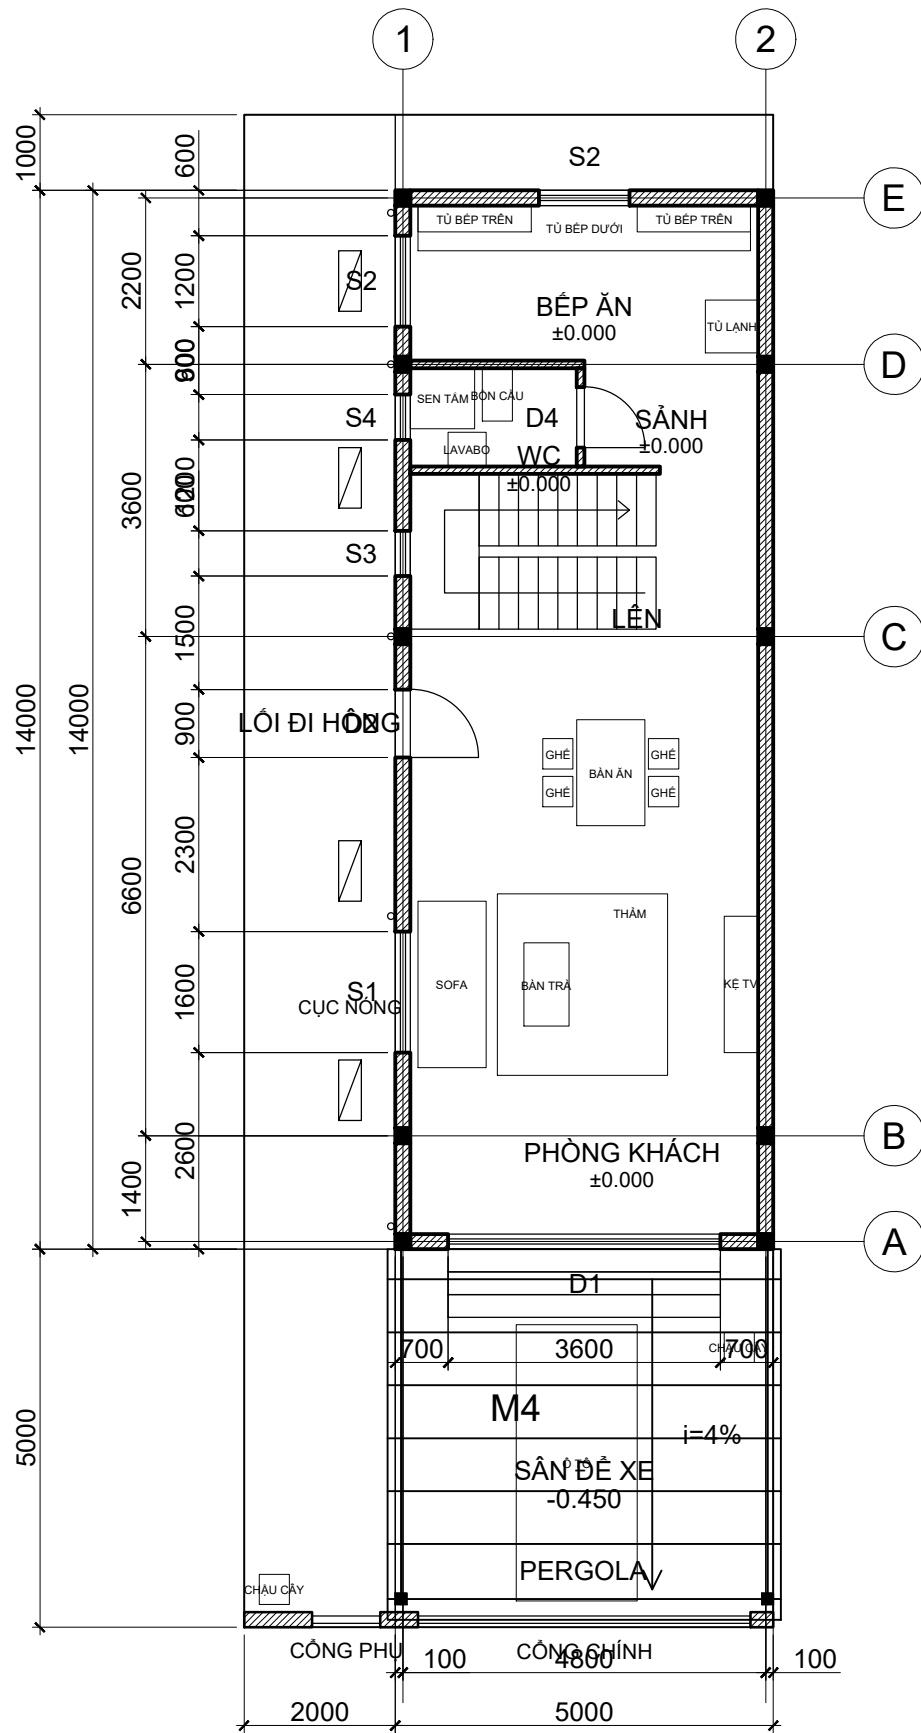


MẶT BẰNG TẦNG 1 VÀ SÂN
TỶ LỆ 1/100

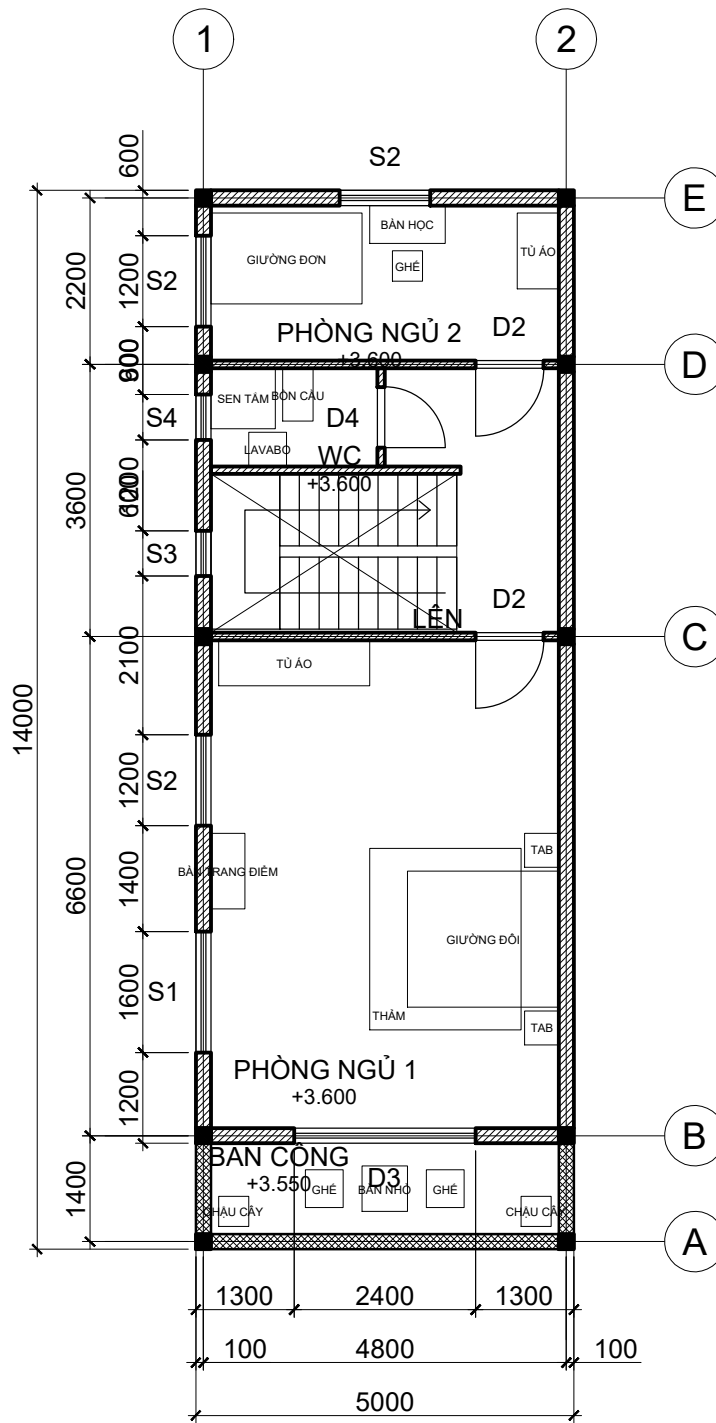

MẶT BẰNG TẦNG 2
TỶ LỆ 1/100

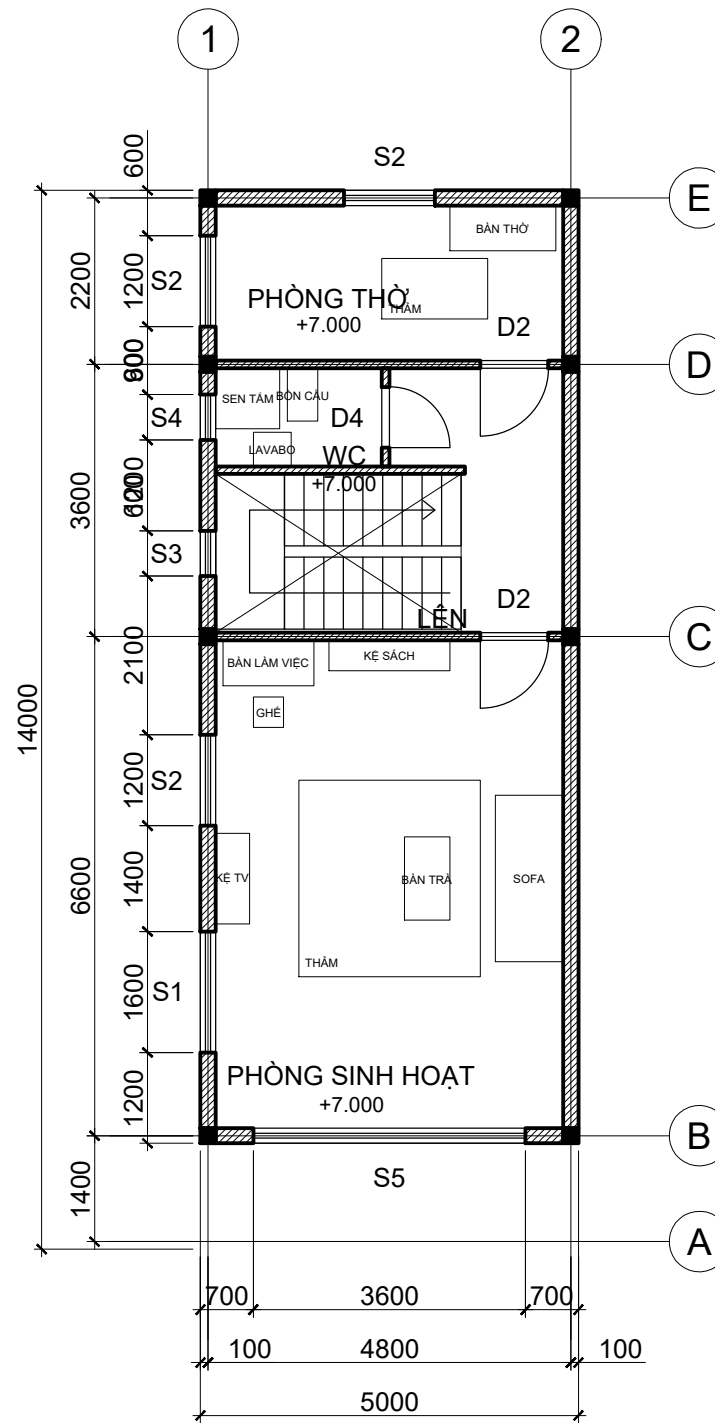

MẶT BẰNG TẦNG 3
TỶ LỆ 1/100

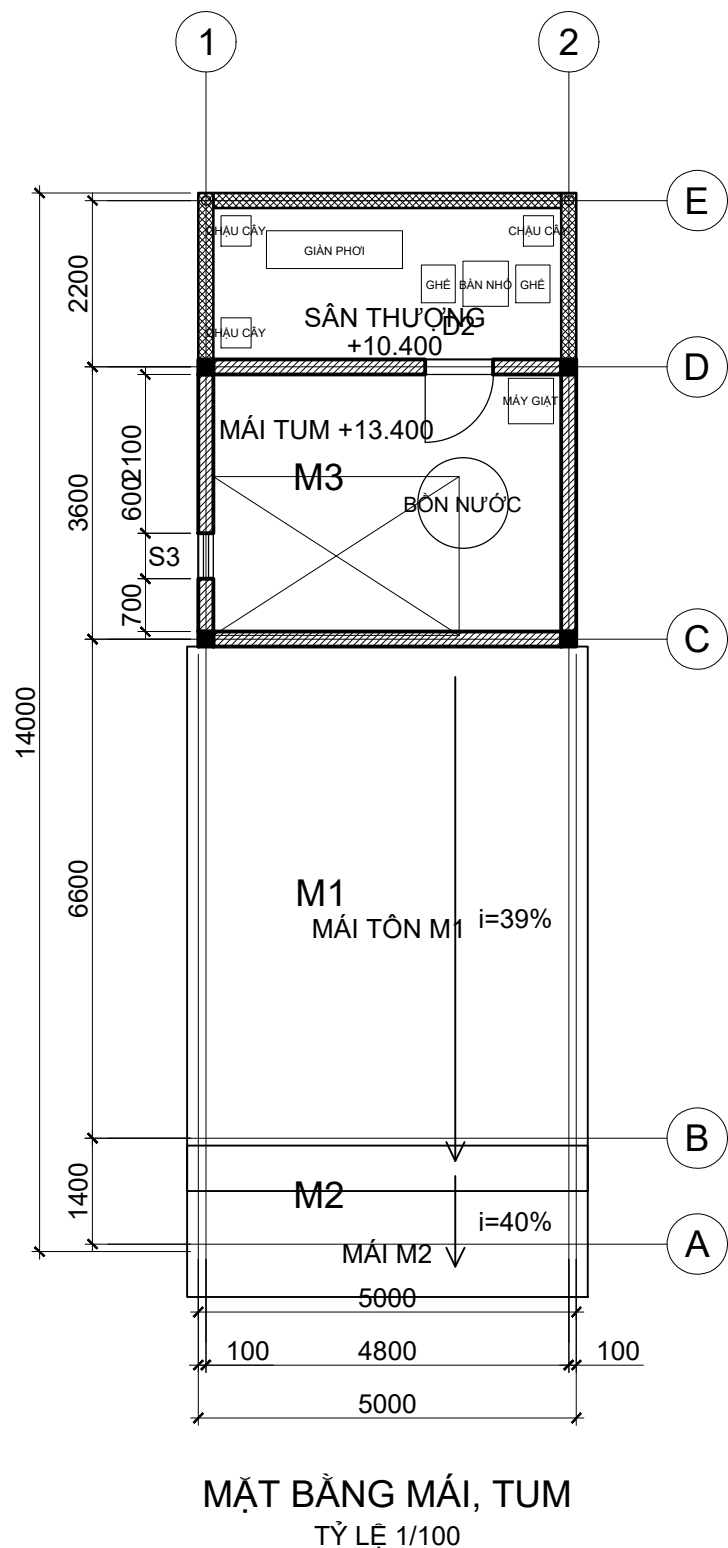

BẢNG THỐNG KÊ CỬA

MÃ	TÊN CỬA	RỘNG	CAO	CAO BÈ	SỐ LƯỢNG
D1	Cửa đi kính khung nhôm 4 cánh	3600	2800	0	1
D2	Cửa đi gỗ 1 cánh	900	2200	0	6
D3	Cửa đi kính lùa 2 cánh	2400	2600	0	1
D4	Cửa đi WC nhôm kính mờ	800	2100	0	3
S1	Cửa sổ kính lớn	1600	2200	400	3
S2	Cửa sổ kính 2 cánh	1200	1400	900	8
S3	Cửa sổ kính đứng cầu thang	600	1800	1200	4
S4	Cửa sổ lật WC	600	600	1500	3
S5	Cửa sổ kính băng	3600	1800	600	1

BẢNG CAO ĐỘ

MÔC	CAO ĐỘ (m)
Sân	-0.450
Tầng 1	±0.000
Tầng 2	+3.600
Tầng 3	+7.000
Sân thượng	+10.400
Mái tum	+13.400

BẢNG MÁI (DỐC VỀ PHÍA MẶT TIỀN)

MÃ	TÊN MÁI	ÁP CHO	ĐỈNH (m)	MÉP (m)
M1	Mái tôn dốc 1 phía	Tầng 3	+12.800	+10.000
M2	Mái tôn che ban công	Tầng 2	+7.000	+6.200
M3	Mái bằng tum BTCT	Tum	+13.400	+13.400
M4	Mái pergola tấm polycarbonate	Sân trước	+3.200	+3.000

BẢNG THÔNG SỐ DỰNG HÌNH

THÔNG SỐ	GIÁ TRỊ (mm)
Sân BTCT dày	120
Mái tôn dày (kể xà gồ)	120
Lan can, tường chắn mái cao	1000
Tường chắn mái tum cao	400
Tường rào cao	1800
Cổng cao	1600
Bồn nước cao	1500
Chân bồn nước cao	300
Kim thu sét cao	1500
Cục nóng máy lạnh cao	550
Ông xối lên tới cao độ	10400
Bạc tam cấp cao	150
Chỉ tường đưa ra	50
Xà pergola cao	200

GHI CHÚ VẬT LIỆU HOÀN THIỆN

- Tường tầng 1, 2: sơn nước màu kem
- Tường tầng 3, tum, lan can, tường chắn mái: ốp tấm gỗ nhựa màu nâu
- Cột, chỉ tường ở cột sàn: sơn màu xám nhạt
- Mái M1, M2: tôn sóng màu đỏ nâu
- Cửa: khung nhôm xám, kính xanh nhạt
- Ông xối: PVC màu xanh lá. Cục nóng máy lạnh: màu trắng
- Pergola, tường rào: khung thép sơn nâu đỏ, mái tấm polycarbonate
- Sân, lối đi: bê tông xám. Bồn nước: inox

Phương án kiến trúc mẫu để dựng 3D; kết cấu chưa tính toán, cần kỹ sư duyệt.



MẶT ĐỨNG CHÍNH (TRỤC 1-2)
TỶ LỆ 1/100



MẶT ĐỨNG BÊN (NHÌN TỪ LỐI ĐI HÔNG)
TỶ LỆ 1/100

Tường tầng 1, 2: sơn nước màu kem
Tường tầng 3, tum, lan can, tường chắn mái: ốp tấm gỗ nhựa màu nâu
Cột, chỉ tường ở cốt sàn: sơn màu xám nhạt
Mái M1, M2: tôn sóng màu đỏ nâu


+13.400 ▽
+12.800 ▽

+10.400 ▽

+7.000 ▽

+3.600 ▽

±0.000 ▽
-0.450 ▽

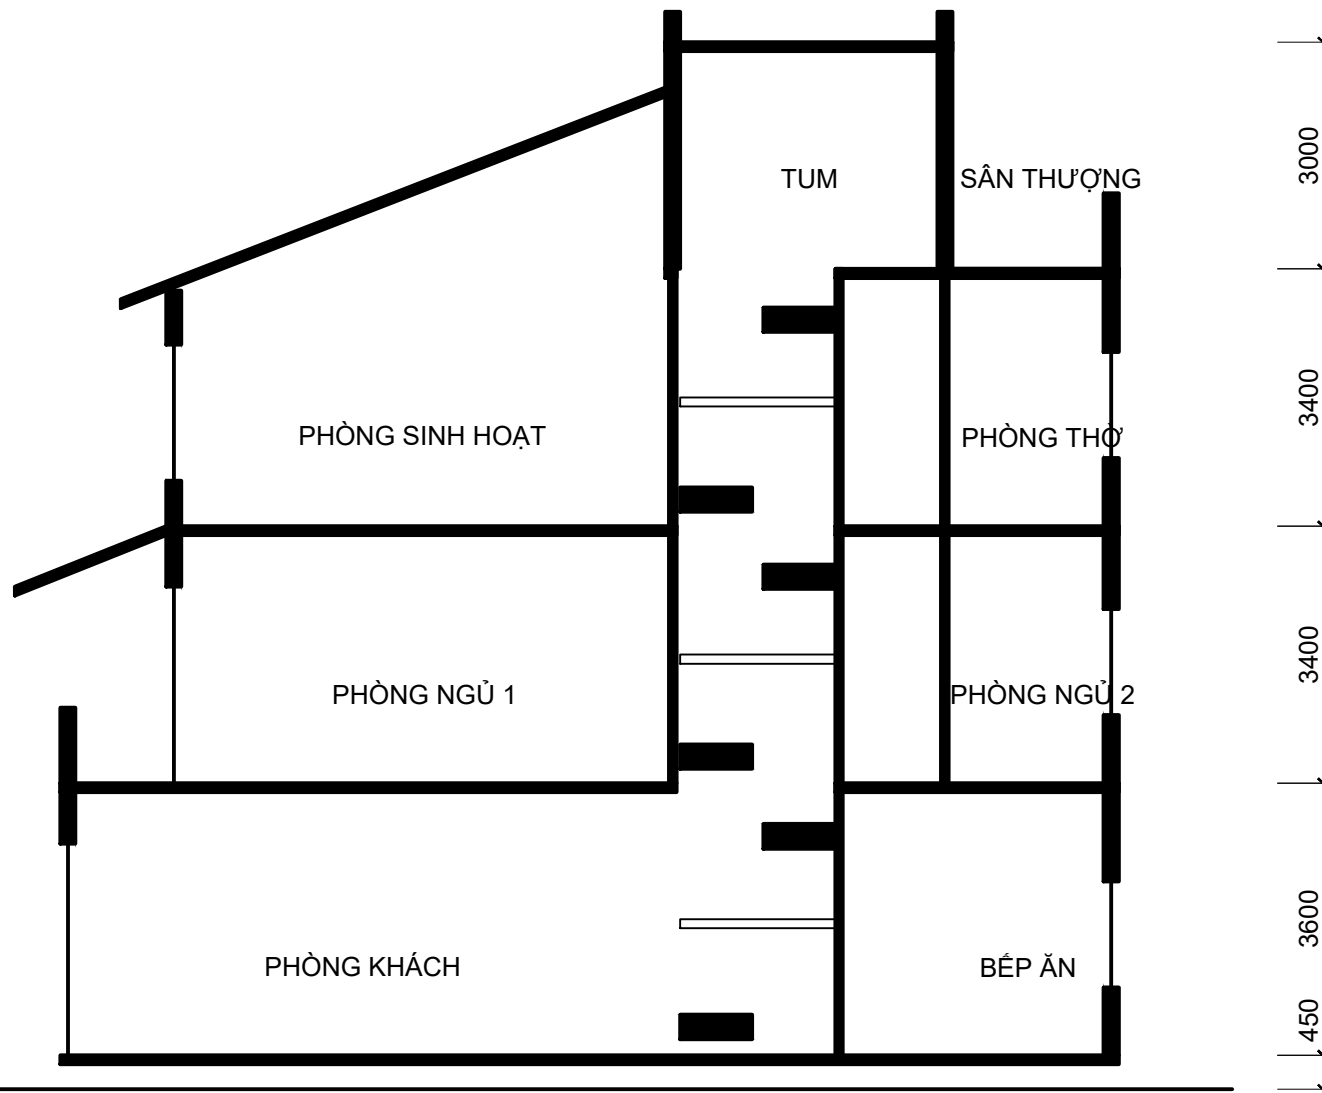

MẶT CẮT 1-1 (CẮT TẠI X = 2700)
TỶ LỆ 1/100